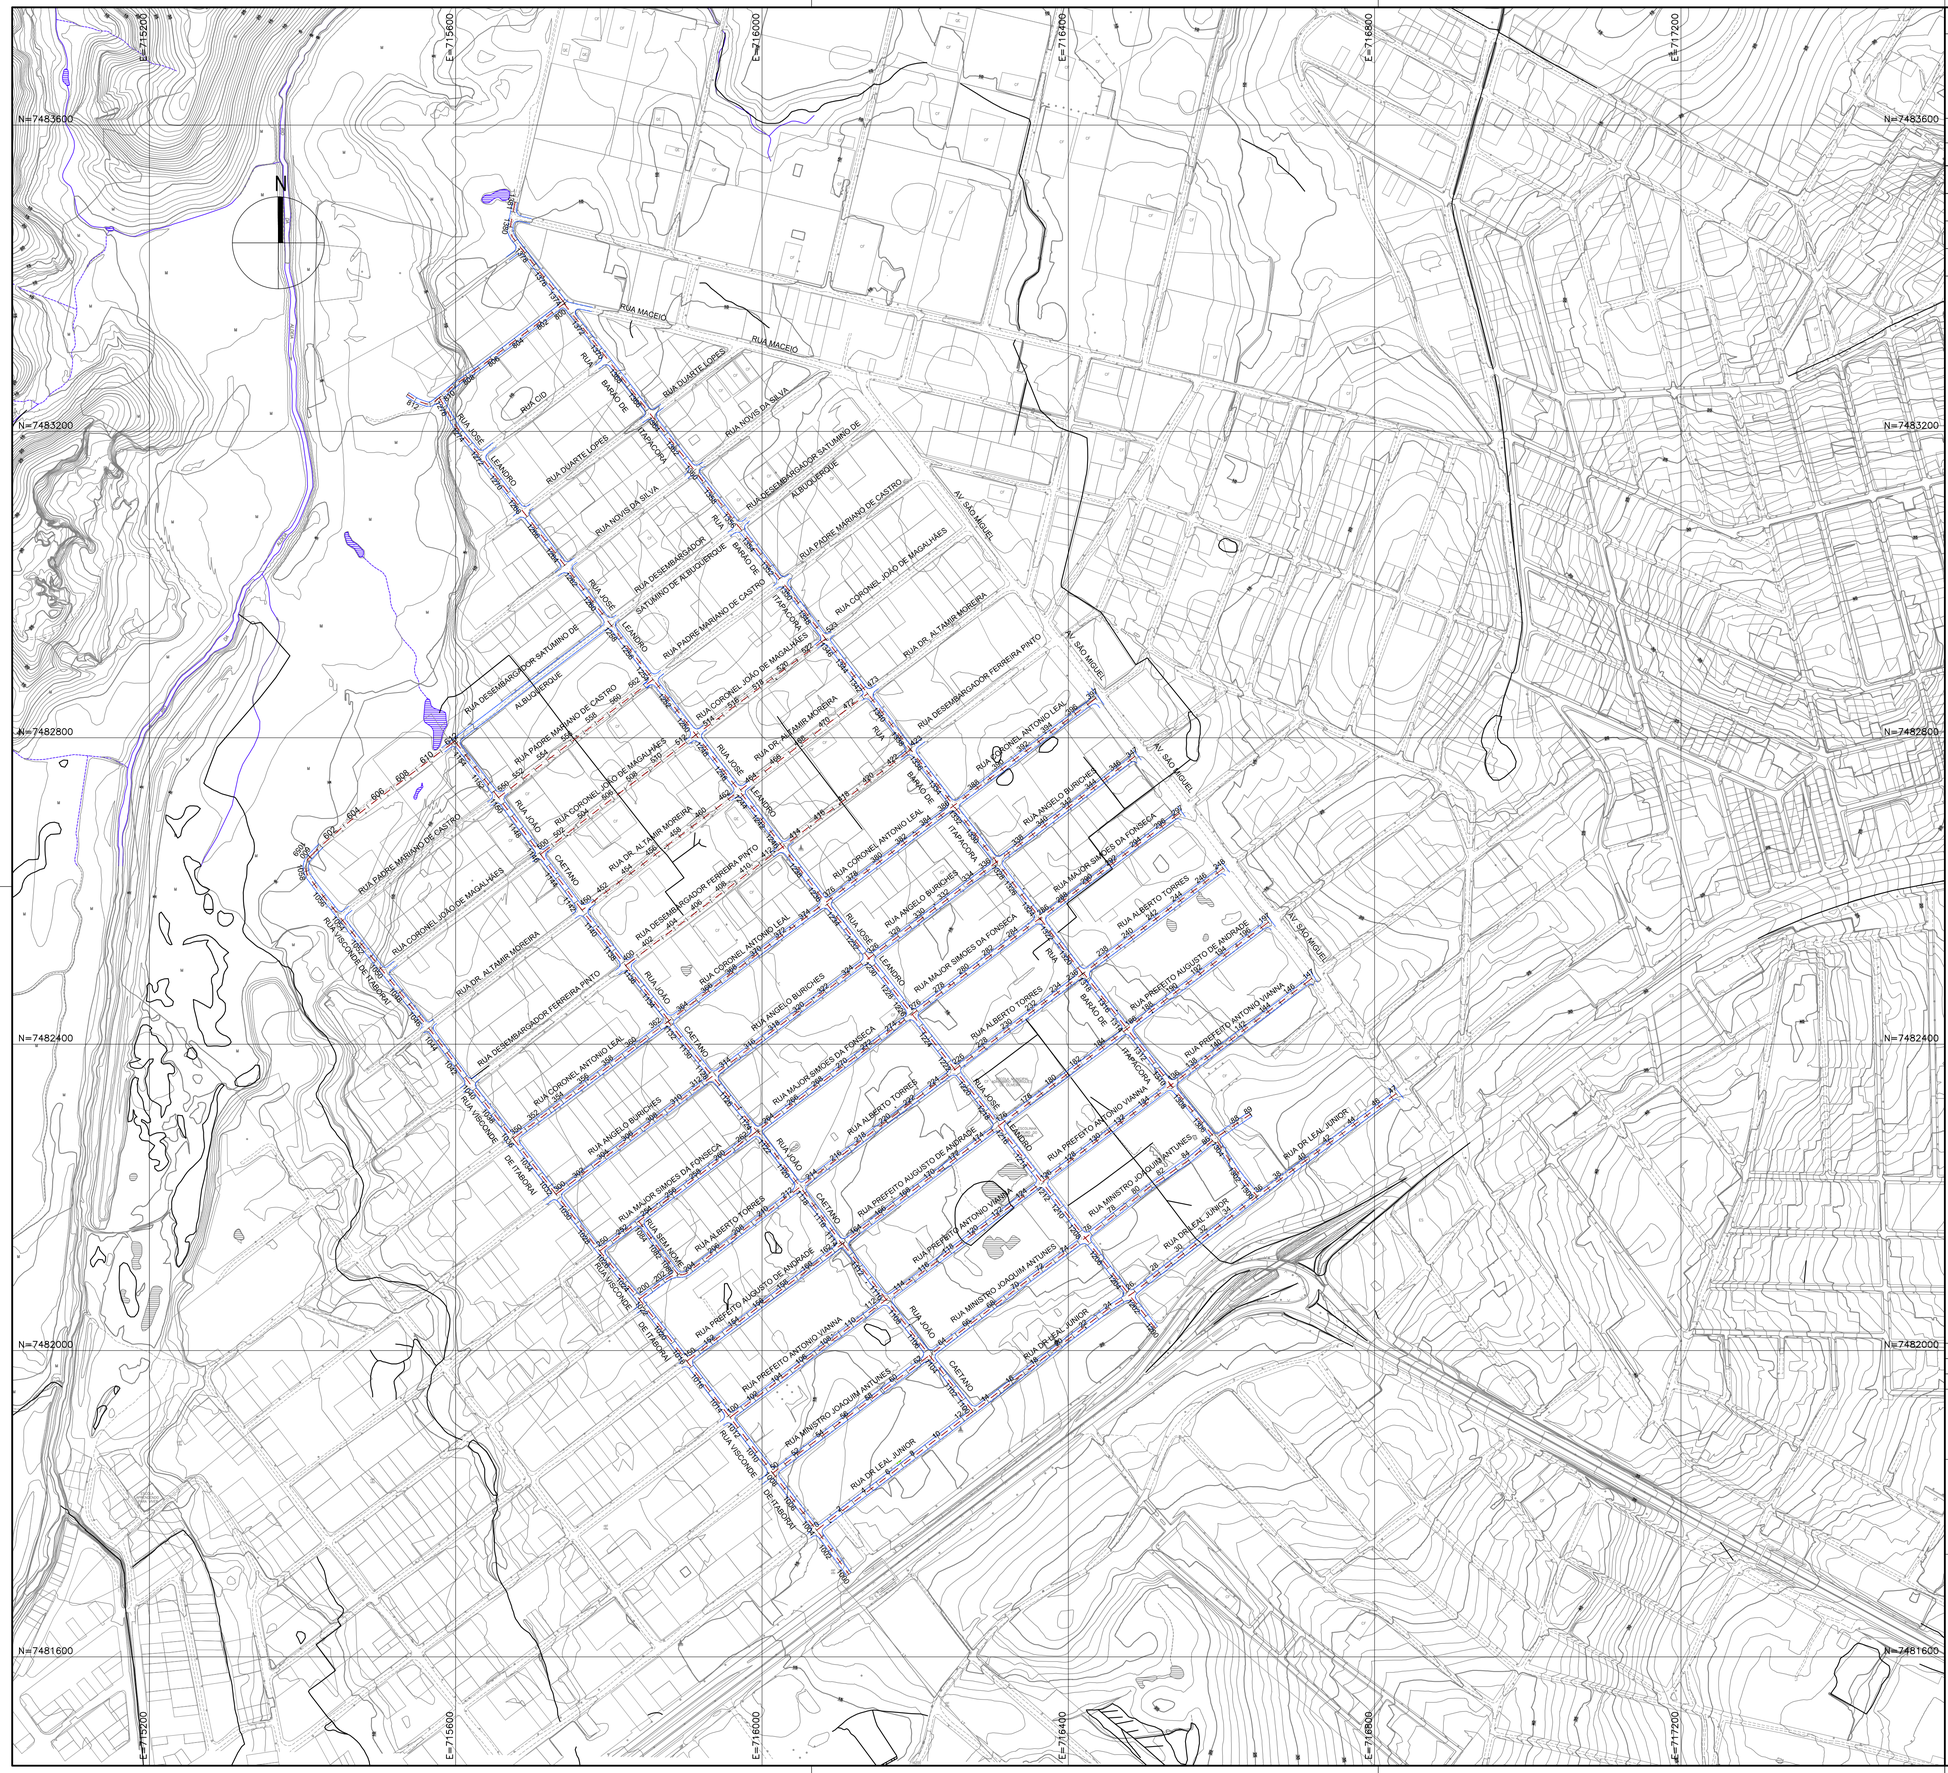


NOTAS GERAIS

1. **DIMENSÕES EM METRO, SALVO INDICAÇÃO CONTRÁRIA.**
2. **AS COTAS FORAM RETIRADAS DO LEVANTAMENTO TOPOGRÁFICO**

LEGENDA

REPRESENTAÇÃO	DESCRIÇÃO
	EIXO PROJETADO
PC	PONTO DE CURVA
PI	PONTO DE INFLEXÃO
PT	PONTO DE TANGÊNCIA

NOTAS:

1. **DIMENSÕES EM METRO, SALVO INDICAÇÃO CONTRÁRIA.**
2. **AS COTAS FORAM RETIRADAS DO LEVANTAMENTO TOPOGRÁFICO**

REVISÃO	DATA	DESCRIÇÃO	PROJ.	VERIF.	APROV.	ASS.
01	19/09/2024	Revisão de Greides				
00	27/08/2024	Emissão Inicial				

CONSTRUTORA - LYTORÂNEA

Secretaria das Cidades

GOVERNO DO ESTADO RIO DE JANEIRO

GESTOR

FISCAL

FISCAL

ELABORAÇÃO DE PROJETO EXECUTIVO
OBRAS DE DRENAGEM PLUVIAL, PAVIMENTAÇÃO E SINALIZAÇÃO VIÁRIA NO BAIRRO RETIRO SÃO JOAQUIM - ITABORAÍ - RJ

PROJETO EXECUTIVO

PROJETO GEOMÉTRICO
PLANTA GERAL

DESENHO	DISCIPLINA	PRANCHA	REVISÃO
DOUGLAS ALMEIDA	GEOMÉTRICO	GEO	01
COORDENAÇÃO	ESCALA: 1:4000 / DATA: 27/08/2024		
RESPONSÁVEL: ANDRÉ LUIS DA SILVA CREA - 2002100973	ARQUIVO: 2024_SJOAQUIM_PE_GEO_DE_001-R01		